

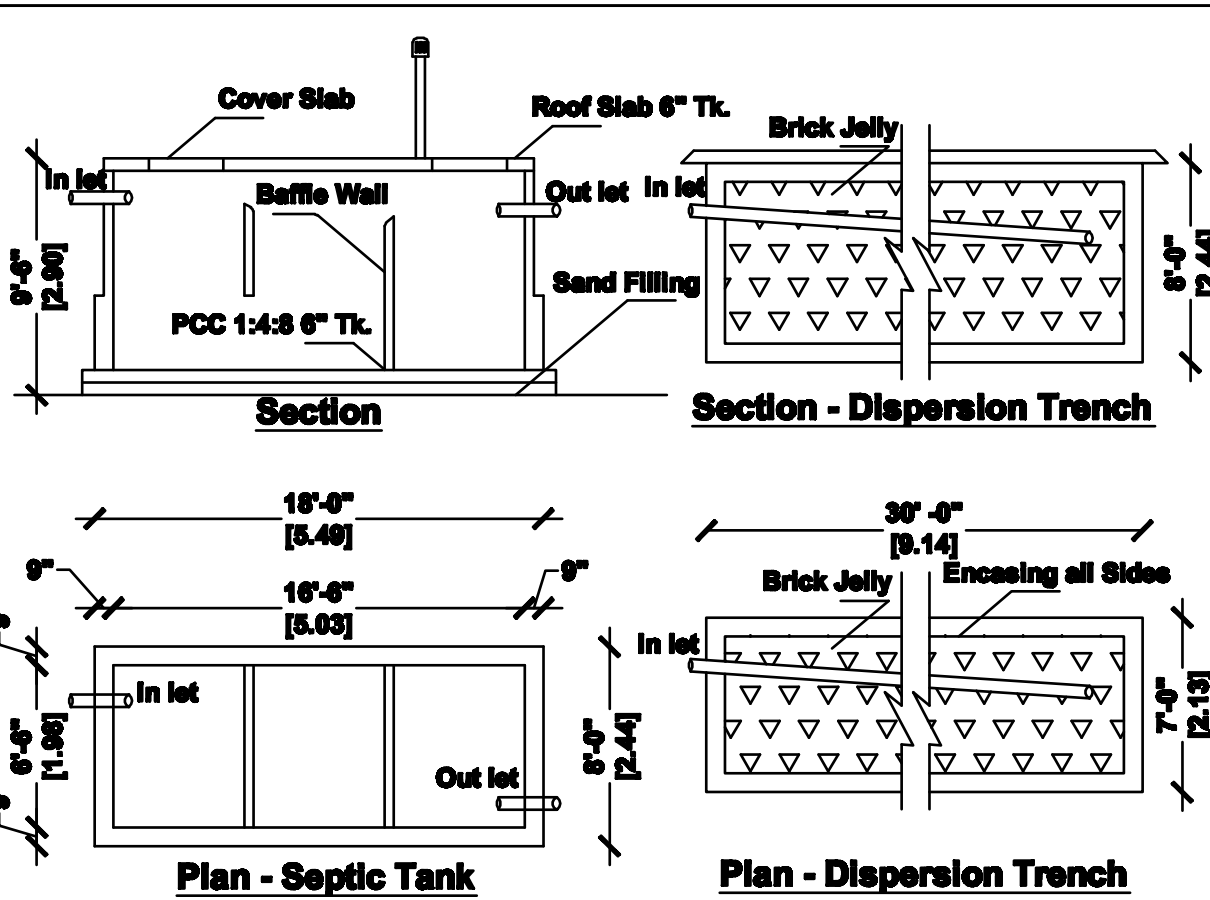
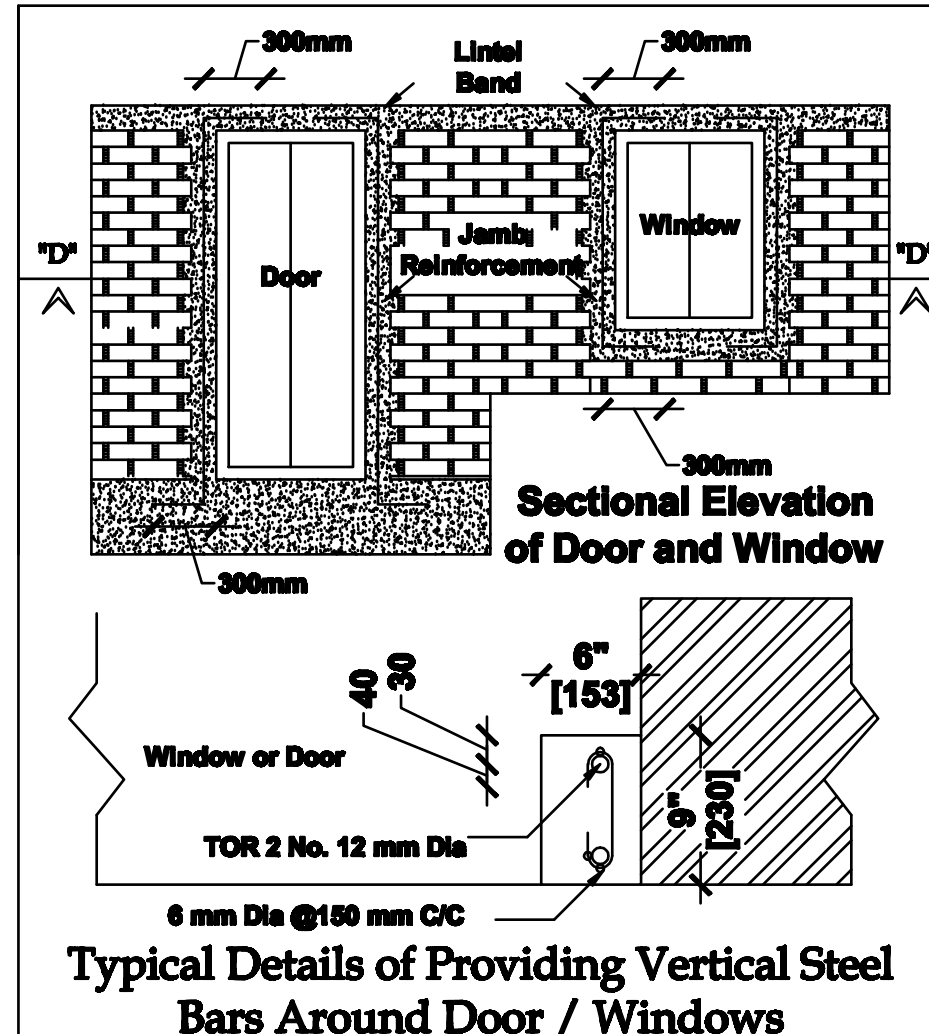
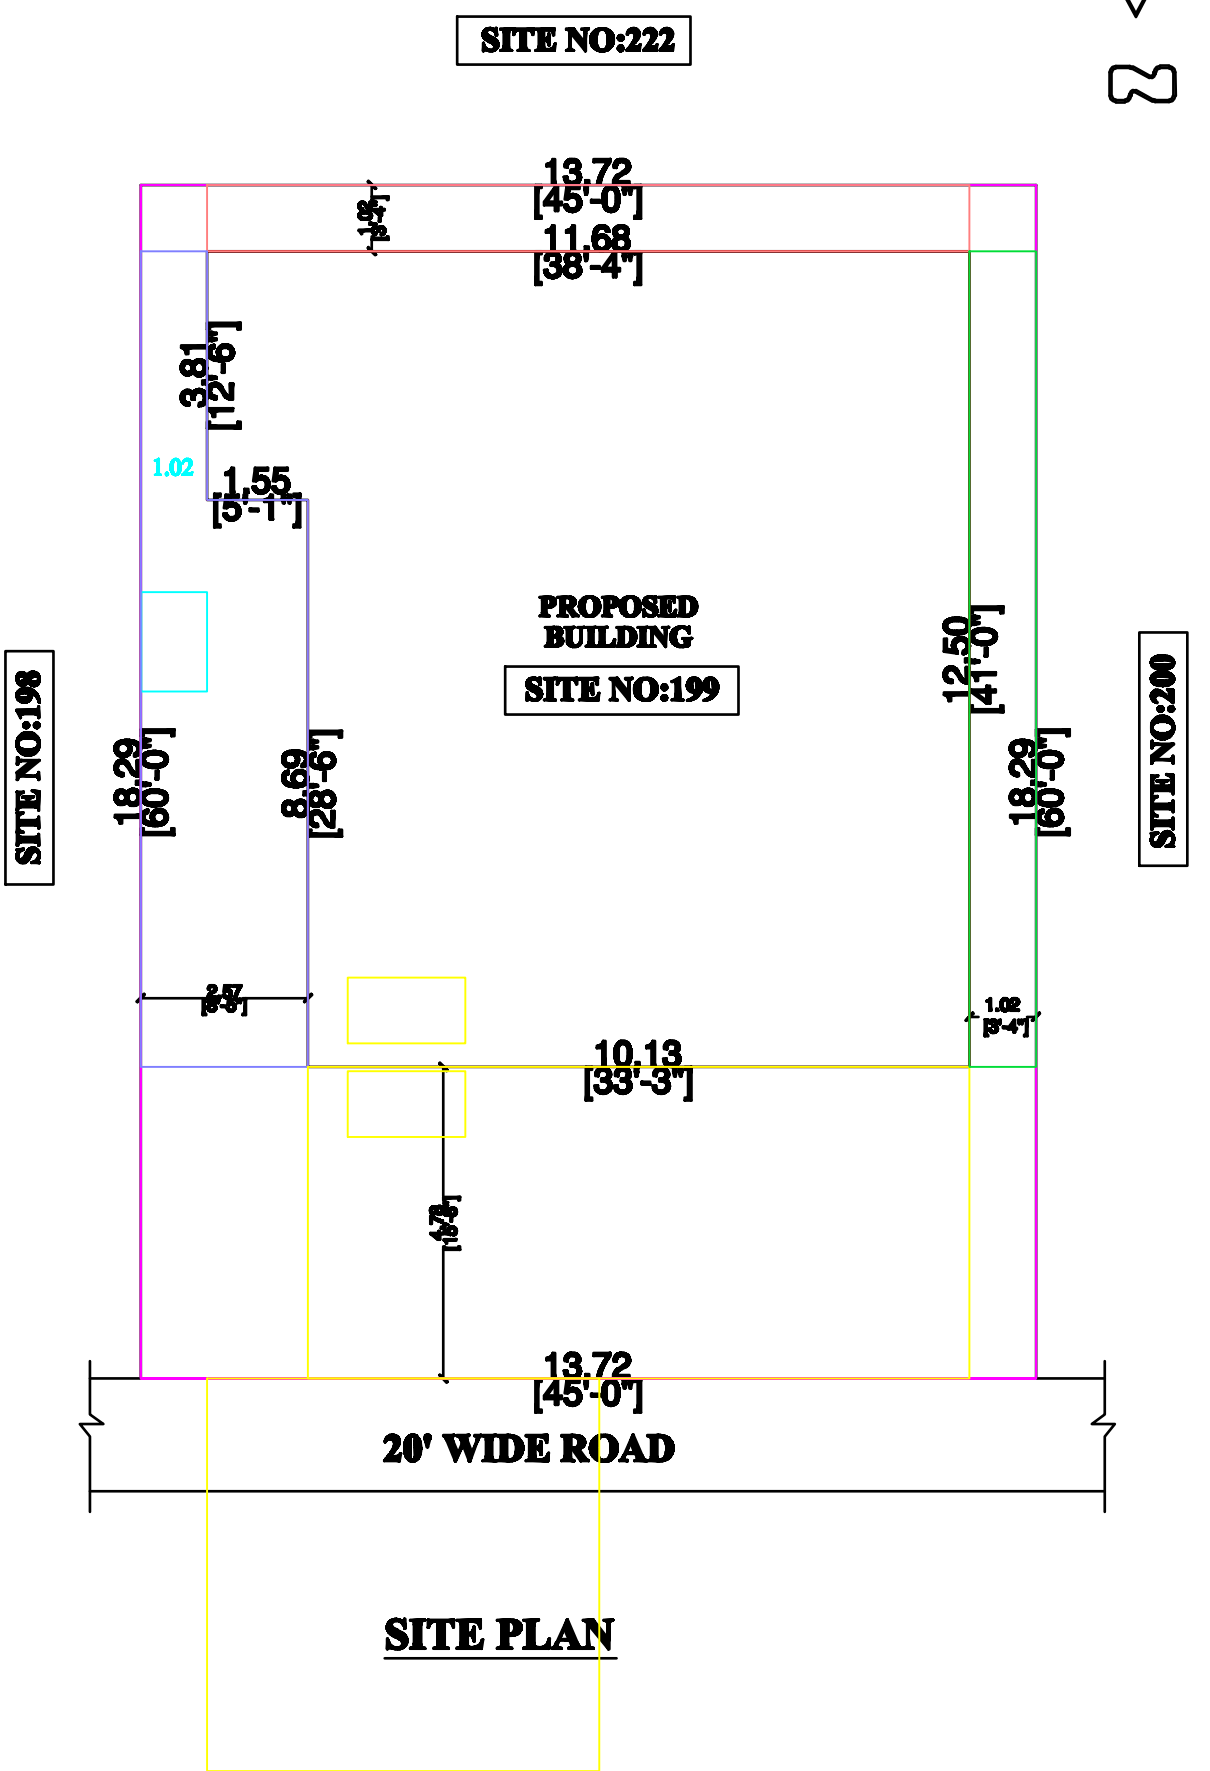
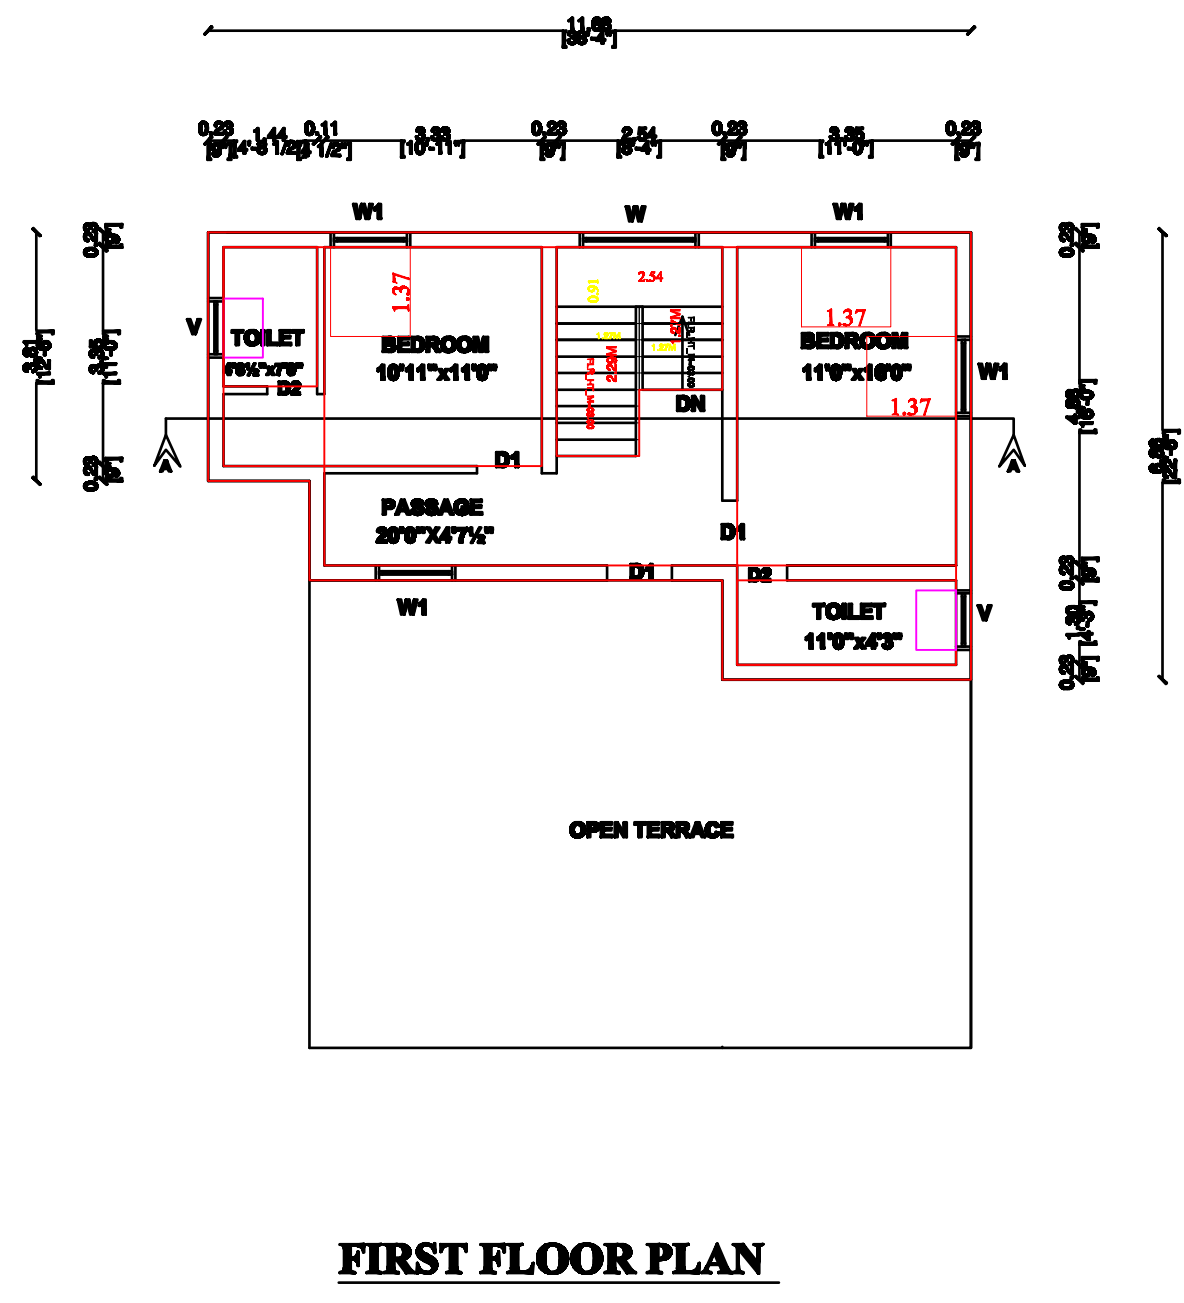
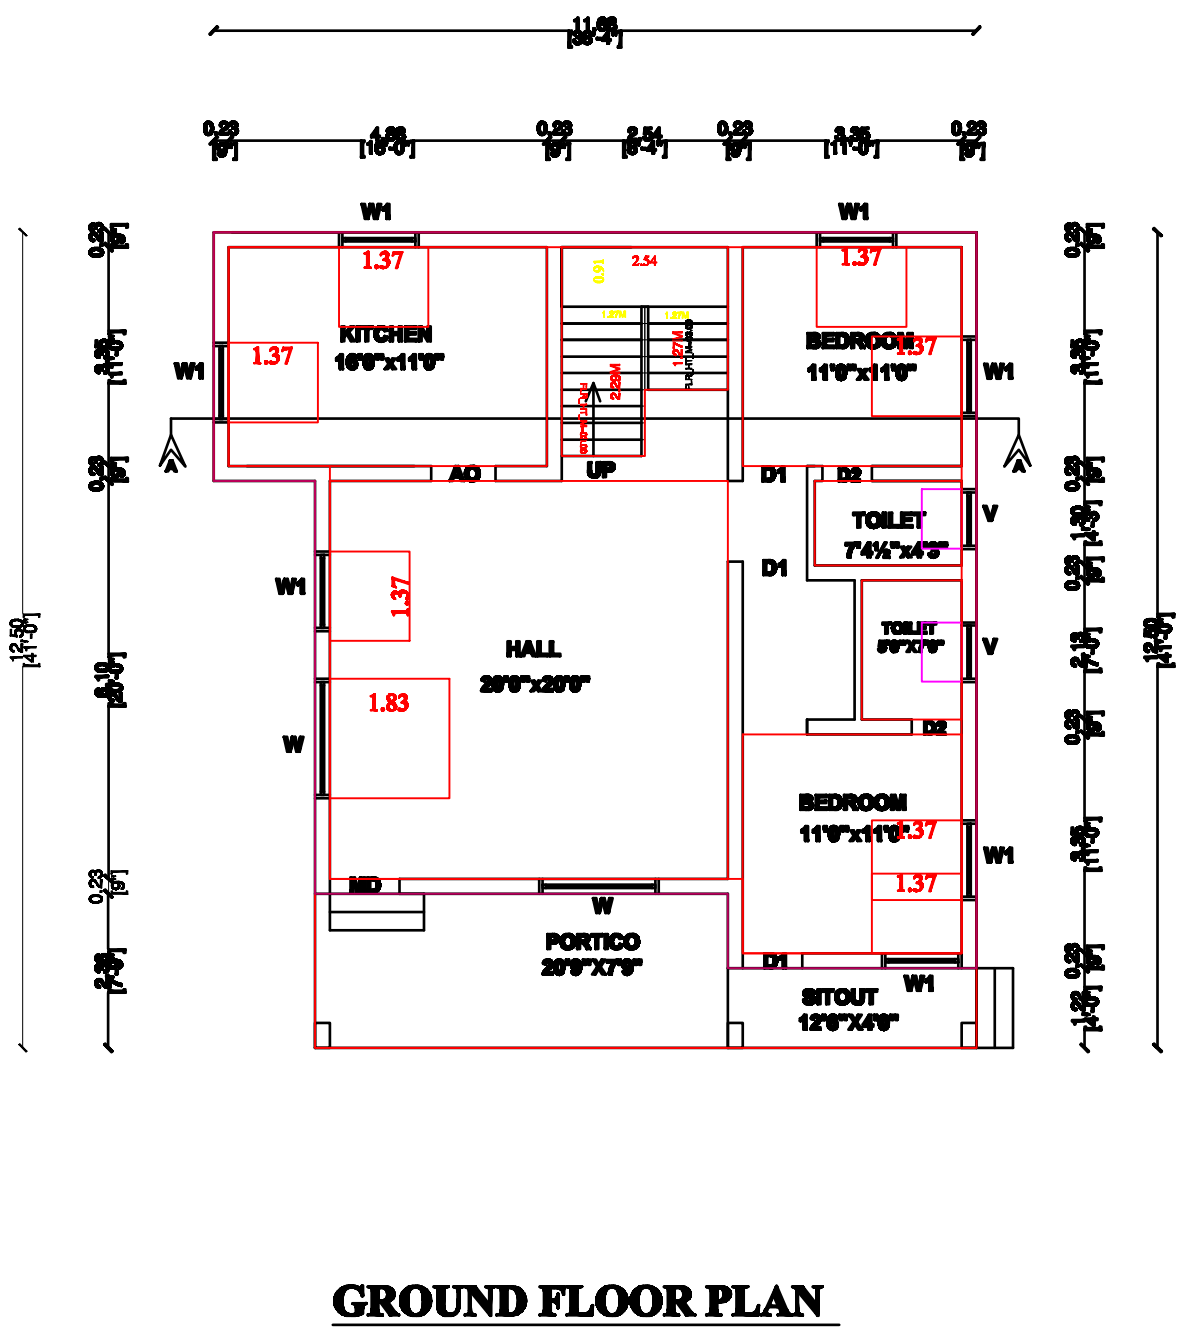
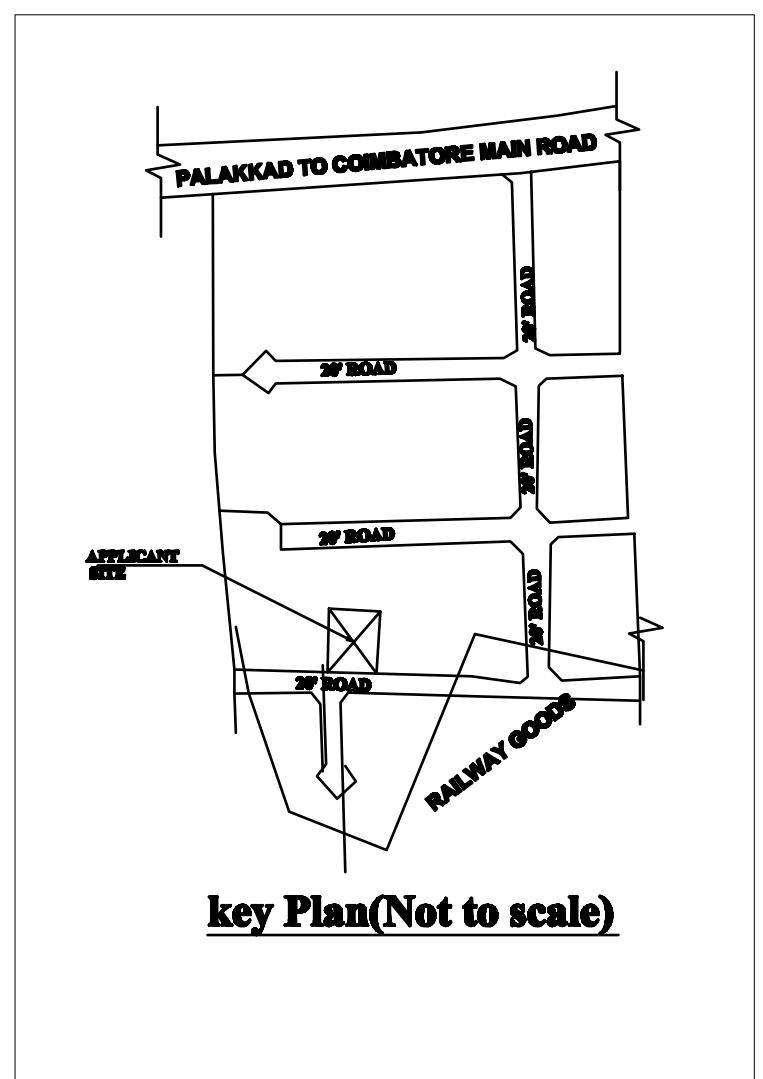


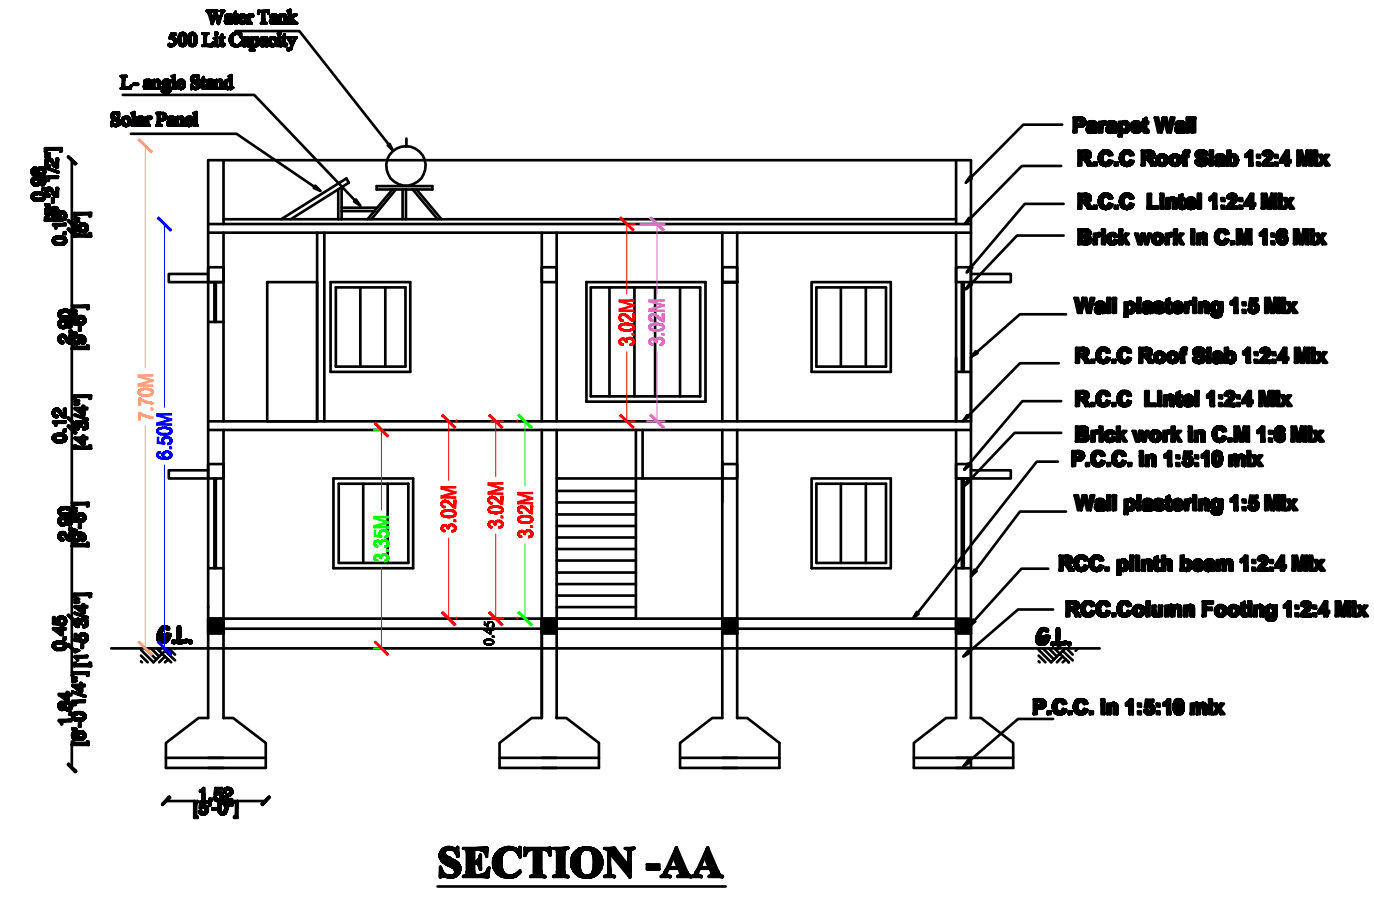



Plan Showing The Proposed Construction of Residential Building
In S.F No:585/1A2, Site No:199, 1980 Before Document, "SRI RAJESHWARI NAGAR",
Ward No:23 , Madukkarai Village & Municipality, Madukkarai Taluk ,
Coimbatore District.

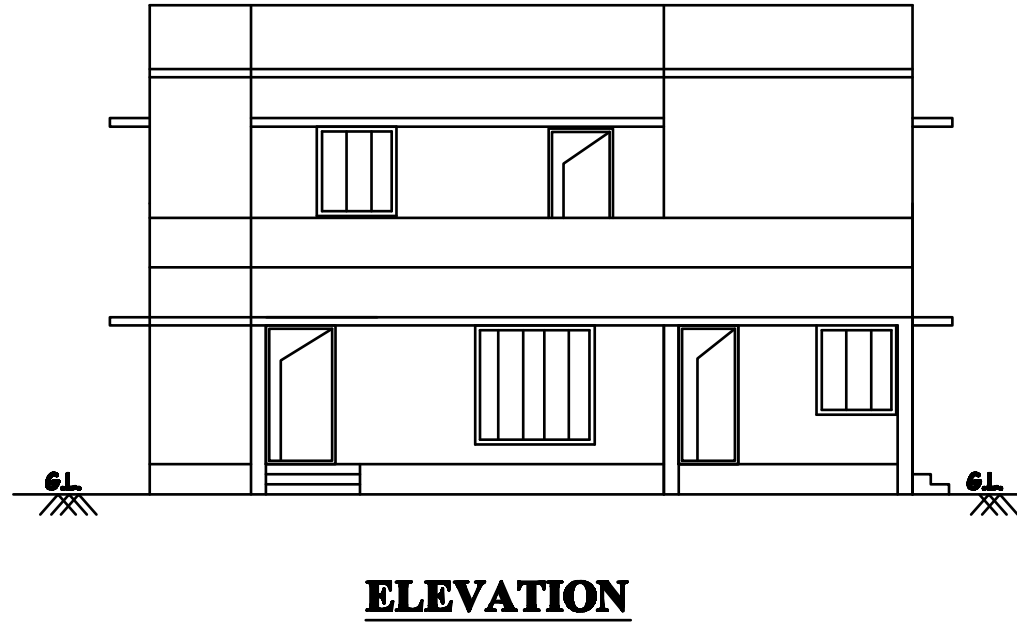

Area Detail	Sq.ft.	Sq.Mt.
Area of the Site	2700.00	250.83
Area of the Prop.Ground Floor	1426.79	132.55
Area of the Prop.First Floor	707.92	65.77
Area of the Open Space	1273.21	118.28

Sanitary Arrangement Proposed Septic Tank 1#			
Scale : 1"=8'0"			
Sym	Joineries	Size in Ft.	Size in Mt.
D	Door	3'6" x 7'0"	1.07 x 2.14
D1	Door	3'3" x 7'0"	1.00 x 2.14
D2	Door	2'6" x 7'0"	0.76 x 2.14
O	Open	3'3" x 7'0"	1.00 x 2.14
W	Window	6'0" x 6'0"	1.82 x 1.82
W1	Window	4'0" x 4'6"	1.22 x 1.37
V	Ventilator	3'0" x 2'0"	0.91 x 0.61

Reference		Staircase Detail
Site Boundary	☐	Rise 0' 7" [0.175]
Prop.Building	☐	Tread 0'10" [0.250]
Ex.layout Road	☐	Width 4' 0" [0.915]

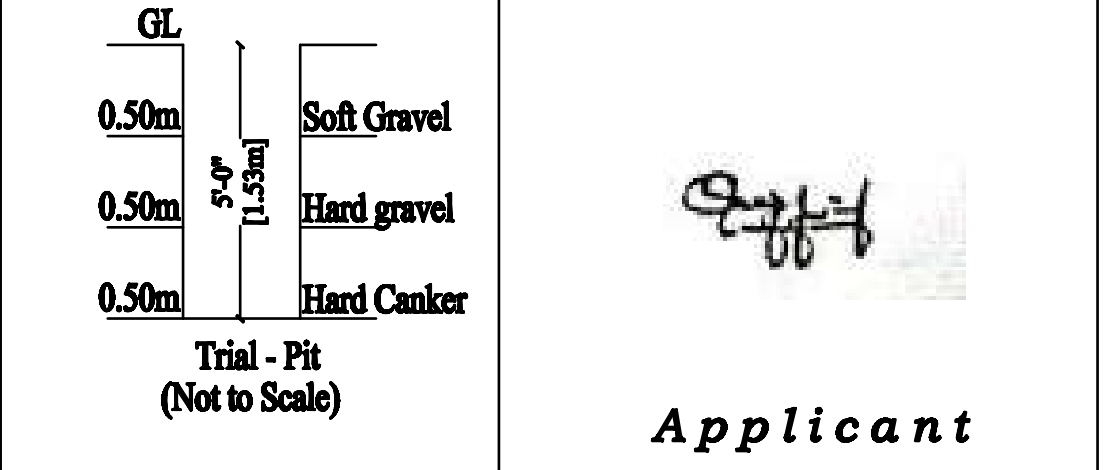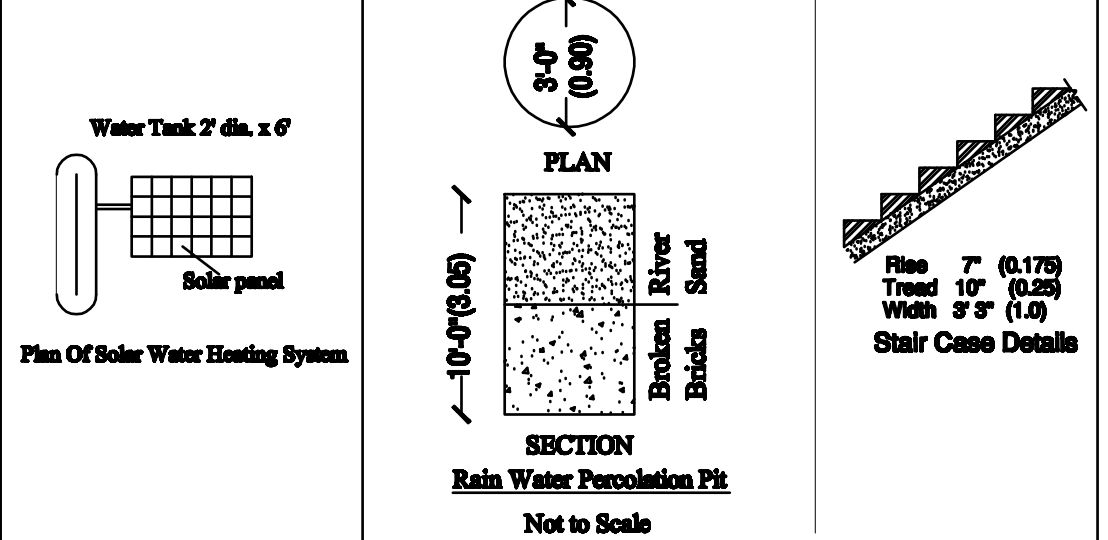

Applicant

Er.K.Satheesh, B.Tech
Govt. Registered Engineer Grade-1(RE)
Reg No.Gr1-00007/2022
Eashaa Vaasthu
Architects & Engineers
T-36A, T-Block, Kovaipudur,
Coimbatore - 641 042.
PH: 99941 44200

Licensed Building Surveyor
Coimbatore